

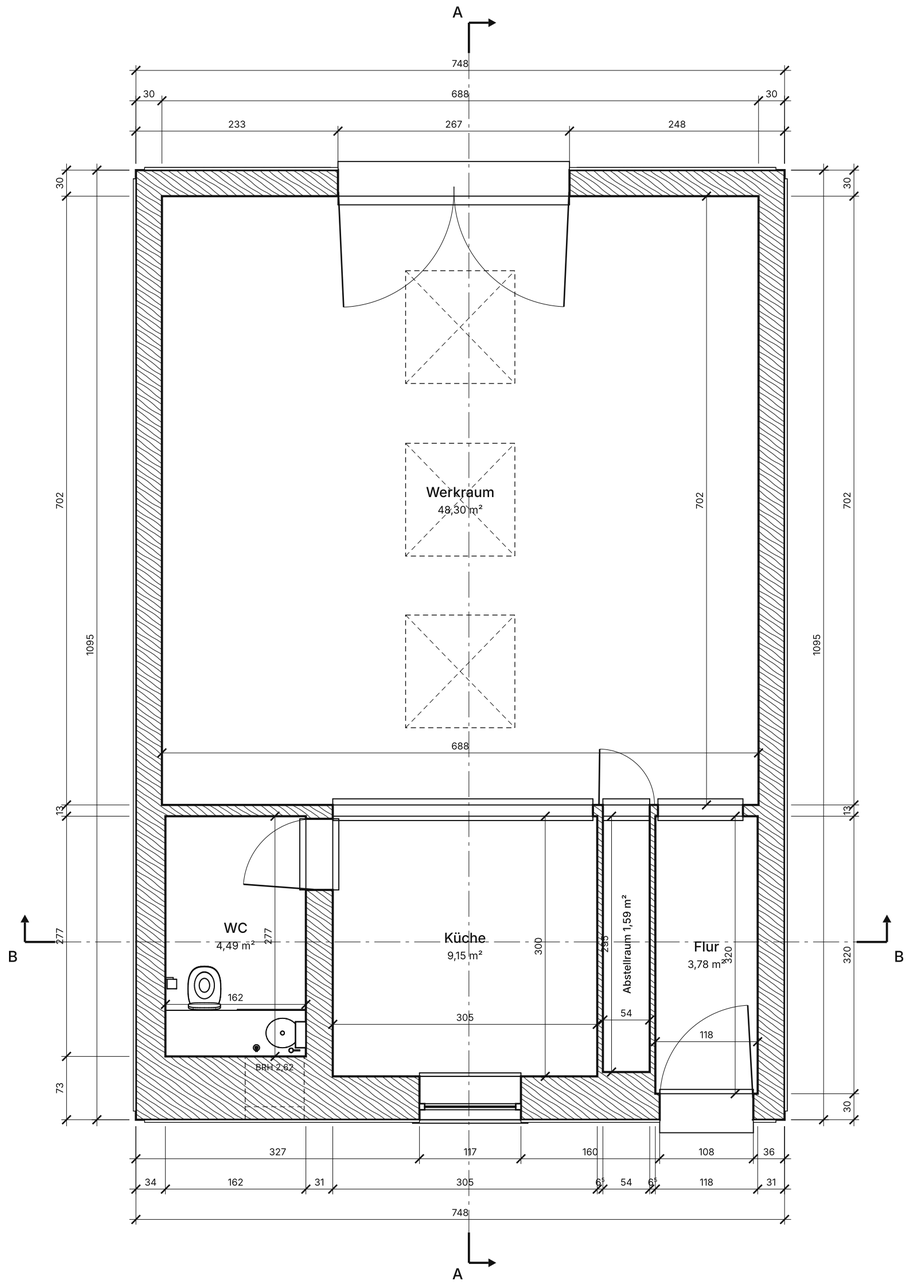


Grundriss M 1:50

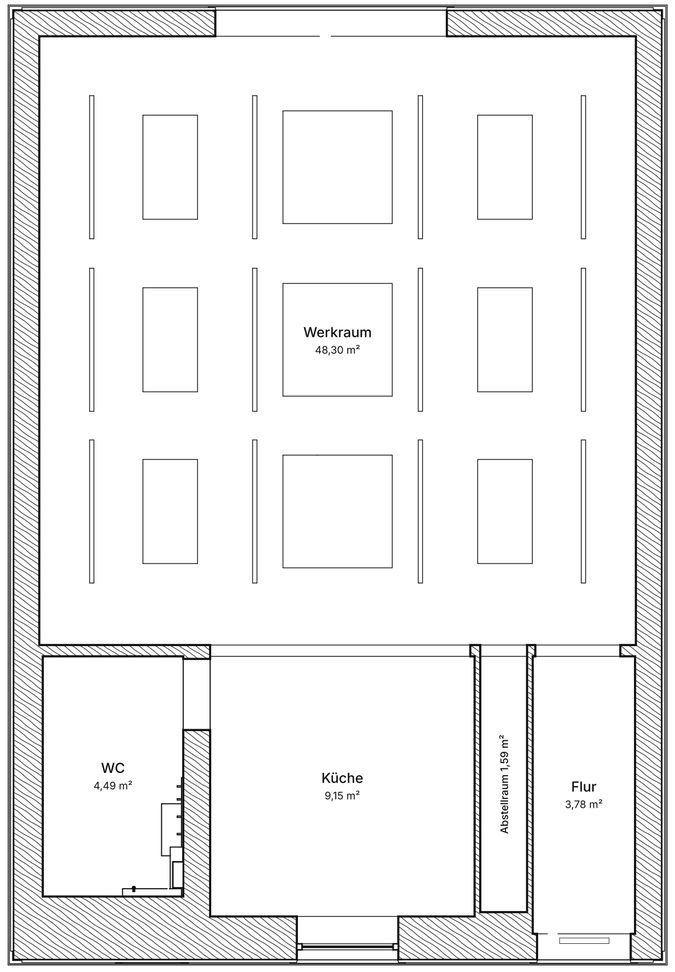

Deckenspiegel M 1:50

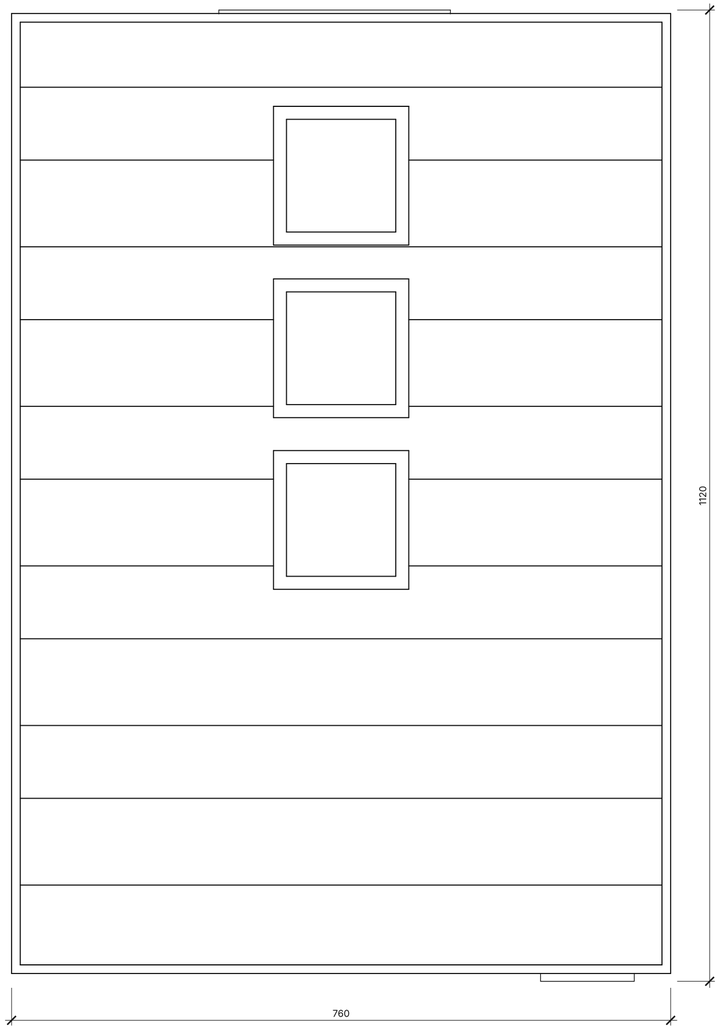

Dachaufsicht M 1:50

YRD.Works
Offenbach am Main


N

Projekt			
FlieKü FNP			
Auftraggeber			
Crespo Foundation			
Planinhalt			
Grundriss, Deckenspiegel, Dachaufsicht			
Planstatus: Bestand	Maßstab: 1:50	Format: A2 · 594×420	Datum: 29.10.2026
Plan-Nr.: **FLK-AP-01**	Index: **A**	Blatt: 1 von 3	Gezeichnet: Ruben Fischer
Geprüft (Name, Datum)		Freigegeben (Name, Datum)	


A	29.10.2026	Erstausgabe

Maße aus 3D-Modell abgeleitet, nicht am Bau aufgemessen.
Flächen: Bodenfläche lt. Modell, keine Berechnung nach DIN 277.
Maße in cm, Höhen in m über OKFF. Darstellung nach DIN 1356-1.

0 1 2 3 4 5 m

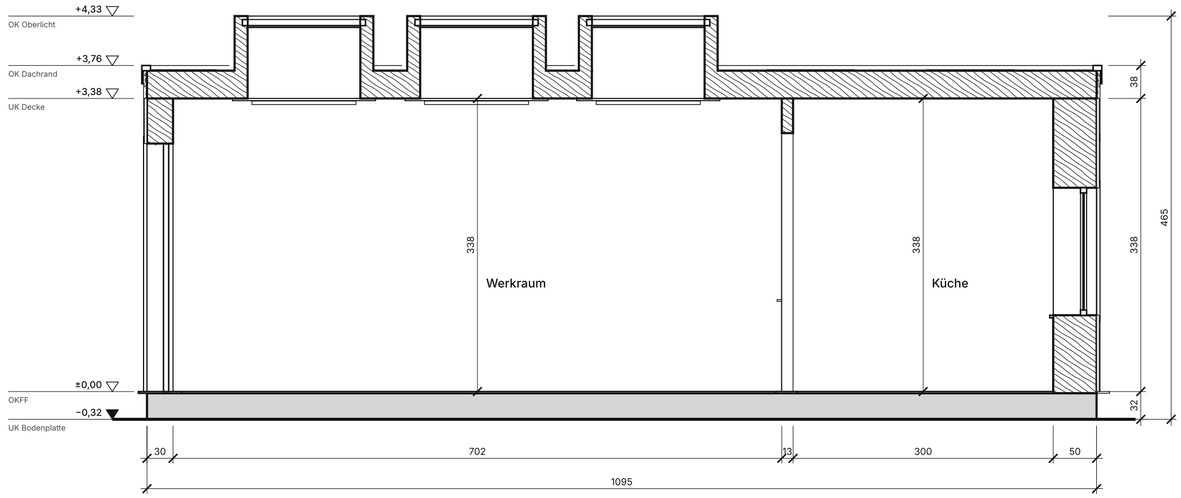

Schnitt A–A M 1:50

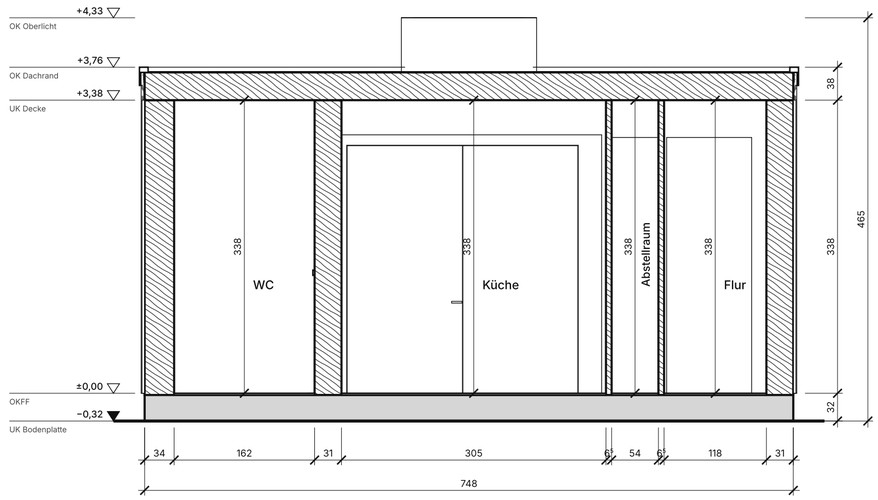

Schnitt B–B M 1:50

YRD.Works

Offenbach am Main


N

Projekt: **FlieKü FNP**			
Auftraggeber: Crespo Foundation			
Planinhalt: **Schnitte A–A, B–B**			
Planstatus: Bestand	Maßstab: 1:50	Format: A2 · 594×420	Datum: 29.10.2026
Plan-Nr.: **FLK-AP-02**	Index: **A**	Blatt: 2 von 3	Gezeichnet: Ruben Fischer
Geprüft (Name, Datum)		Freigegeben (Name, Datum)	


A	29.10.2026	Erstausgabe

Maße aus 3D-Modell abgeleitet, nicht am Bau aufgemessen.
Flächen: Bodenfläche lt. Modell, keine Berechnung nach DIN 277.
Maße in cm, Höhen in m über OKFF. Darstellung nach DIN 1356-1.


0 1 2 3 4 5 m

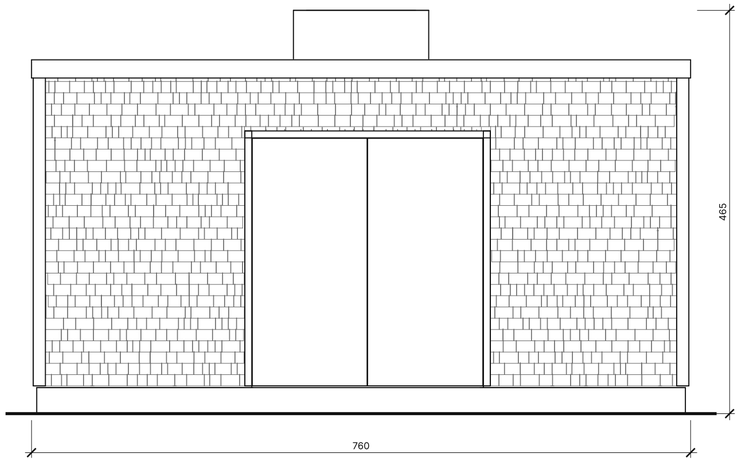


Ansicht Nord M 1:50

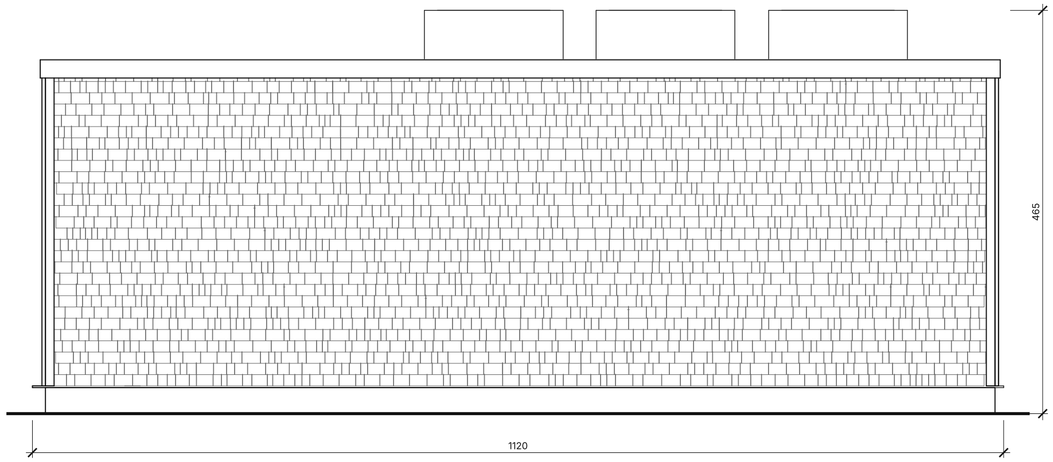

Ansicht Ost M 1:50

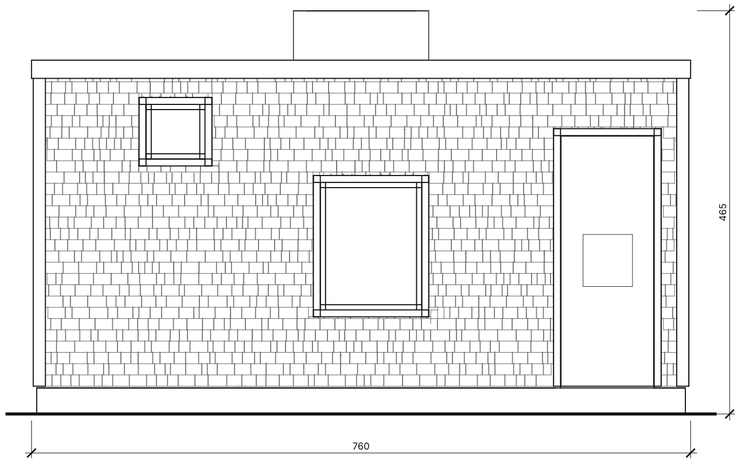

Ansicht Süd M 1:50

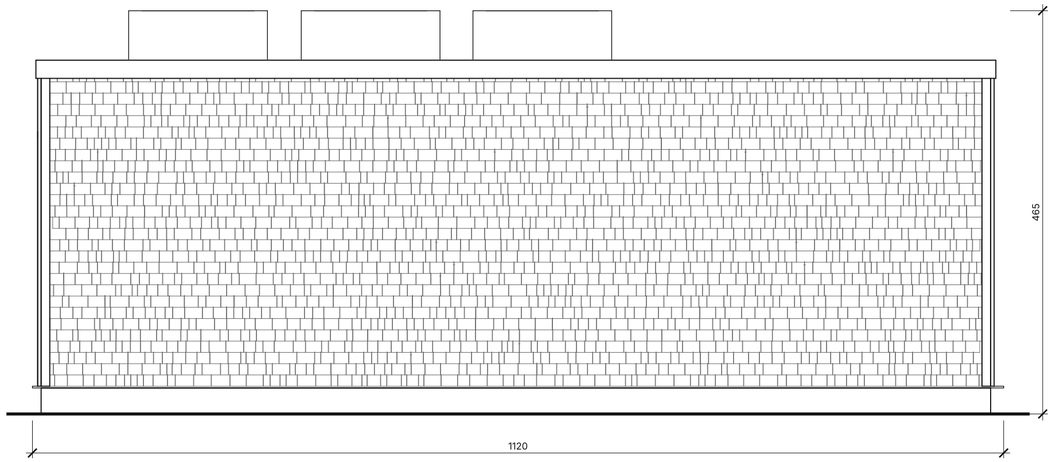

Ansicht West M 1:50

YRD.Works
Offenbach am Main

N

Projekt
FlieKü FNP

Auftraggeber
Crespo Foundation

Planinhalt
Ansichten Nord, Ost, Süd, West

Planstatus	Maßstab	Format	Datum
Bestand	1:50	A2 · 594×420	29.10.2026

Plan-Nr.	Index	Blatt	Gezeichnet
FLK-AP-03	**A**	3 von 3	Ruben Fischer

Geprüft (Name, Datum)	Freigegeben (Name, Datum)

A	29.10.2026	Erstausgabe

Maße aus 3D-Modell abgeleitet, nicht am Bau aufgemessen.
Flächen: Bodenfläche lt. Modell, keine Berechnung nach DIN 277.
Maße in cm, Höhen in m über OKFF. Darstellung nach DIN 1356-1.

0 1 2 3 4 5 m